
PANEL DESIGNATION

PANEL A - MAIN

LOCATION: GARAGE, NORTH WALL

SERVICE	MAIN	BUS RATING	SPACES
120/240V 1Φ 3W	200A MAIN BREAKER	200A	40
MANUFACTURER / MODEL	**FED FROM**	**CIRCUITS**	**SPACE USAGE**
SQUARE D QO140M200	UTILITY METER	28	32 USED / 8 OPEN

CIRCUIT DESCRIPTION	TRIP	CKT
RANGE / OVEN	**40A 2P**	**1**
		3
KITCHEN COUNTERTOP RECEPTACLES (LEFT OF SINK)	**20A** AFCI/GFCI	**5**
KITCHEN COUNTERTOP RECEPTACLES (RIGHT OF SINK)	**20A** AFCI/GFCI	**7**
DISHWASHER	**20A** TIED	**9**
GARBAGE DISPOSAL (MWBC WITH CKT 9)	**20A** TIED	**11**
REFRIGERATOR	**20A**	**13**
BEDROOM 1	**15A** AFCI	**15**
BEDROOM 2	**15A** AFCI	**17**
PRIMARY BEDROOM	**15A** AFCI	**19**
BATHROOMS RECEPTACLES	**20A** GFCI	**21**
LIVING ROOM & DINING ROOM	**15A** AFCI	**23**
MICROWAVE	**20A**	**25**
SMOKE DETECTORS	**15A**	**27**
EV CHARGER (GARAGE)	**50A 2P**	**29**
		31
SPACE	—	**33**
SPACE	—	**35**
SPACE	—	**37**
SPACE	—	**39**

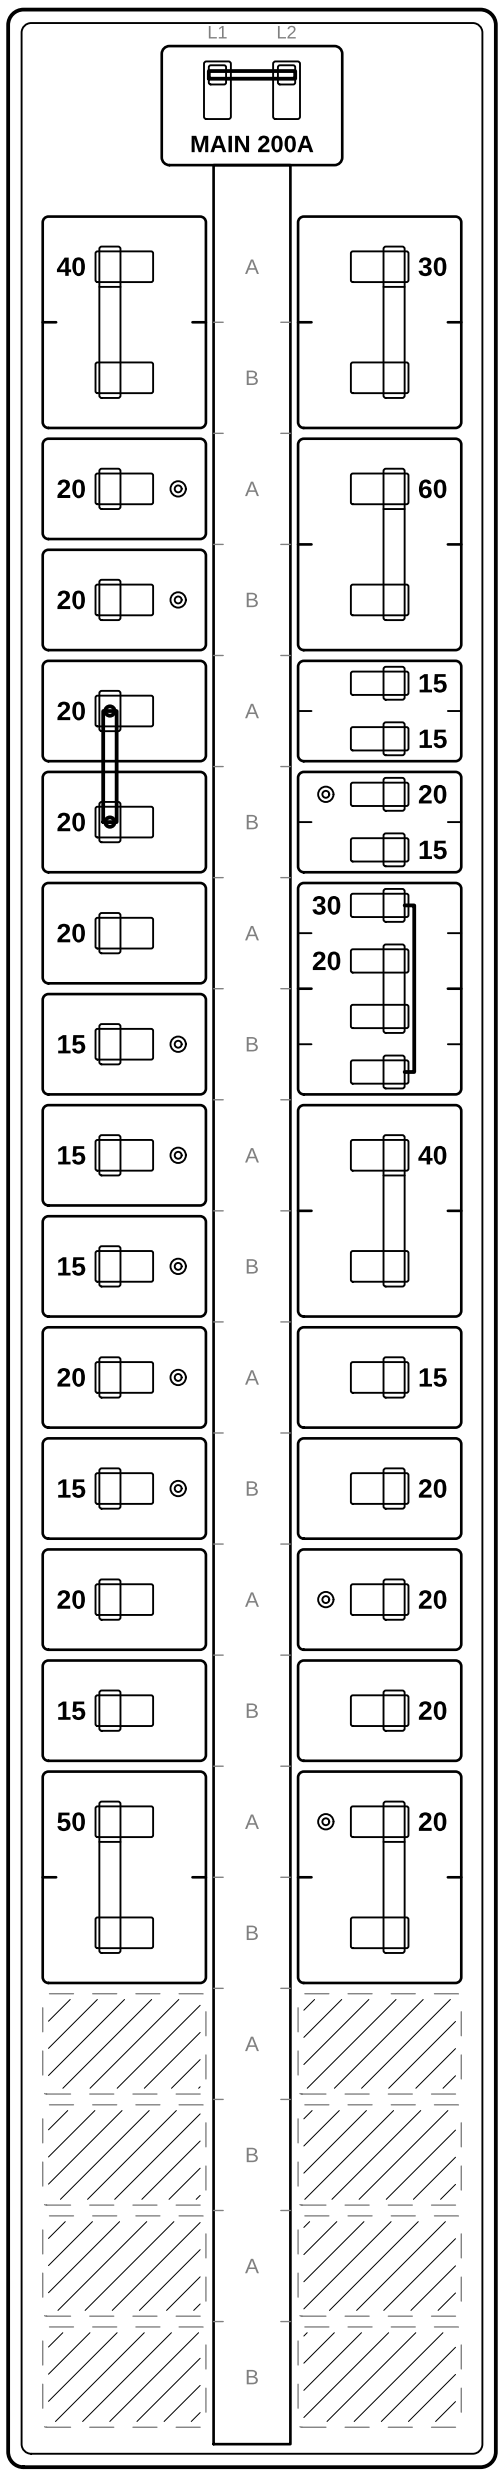

CKT	TRIP	CIRCUIT DESCRIPTION
2	**30A 2P**	CLOTHES DRYER
4		
6	**60A 2P**	SUBPANEL B - DETACHED WORKSHOP
8		
10A	**15A**	HALL & STAIR LIGHTING
10B	**15A**	FRONT PORCH LIGHTS
12A	**20A GFCI**	GARAGE RECEPTACLES
12B	**15A**	GARAGE DOOR OPENER
14A	**30A 2P**	OUTER 14A/16B WATER HEATER
14B		
16A	**20A 2P**	INNER 14B/16A WELL PUMP
16B		
18	**40A 2P**	A/C CONDENSER
20		
22	**15A**	FURNACE / AIR HANDLER
24	**20A**	LAUNDRY RECEPTACLE
26	**20A** GFCI	EXTERIOR RECEPTACLES
28	**20A**	SPARE
30	**20A 2P** SURGE	WHOLE-HOUSE SURGE PROTECTOR
32		
34	—	SPACE
36	—	SPACE
38	—	SPACE
40	—	SPACE

NOTES

1. Circuits 9 and 11 are a multi-wire branch circuit sharing a neutral; handle tie required.
2. Verify circuit identification with a circuit tracer before working on any circuit.
3. Grounding electrode: two ground rods, 6 ft apart, at the meter base.

PROJECT / PROPERTY

1234 EXAMPLE STREET

DRAWING TITLE

PANEL A - MAIN — PANEL DIRECTORY

DRAWN BY	DATE	SCALE
D. PANZINO	2026-10-15	NONE

SIZE	DWG NO.	REV	SHEET
B	E-101	**A**	1 OF 2