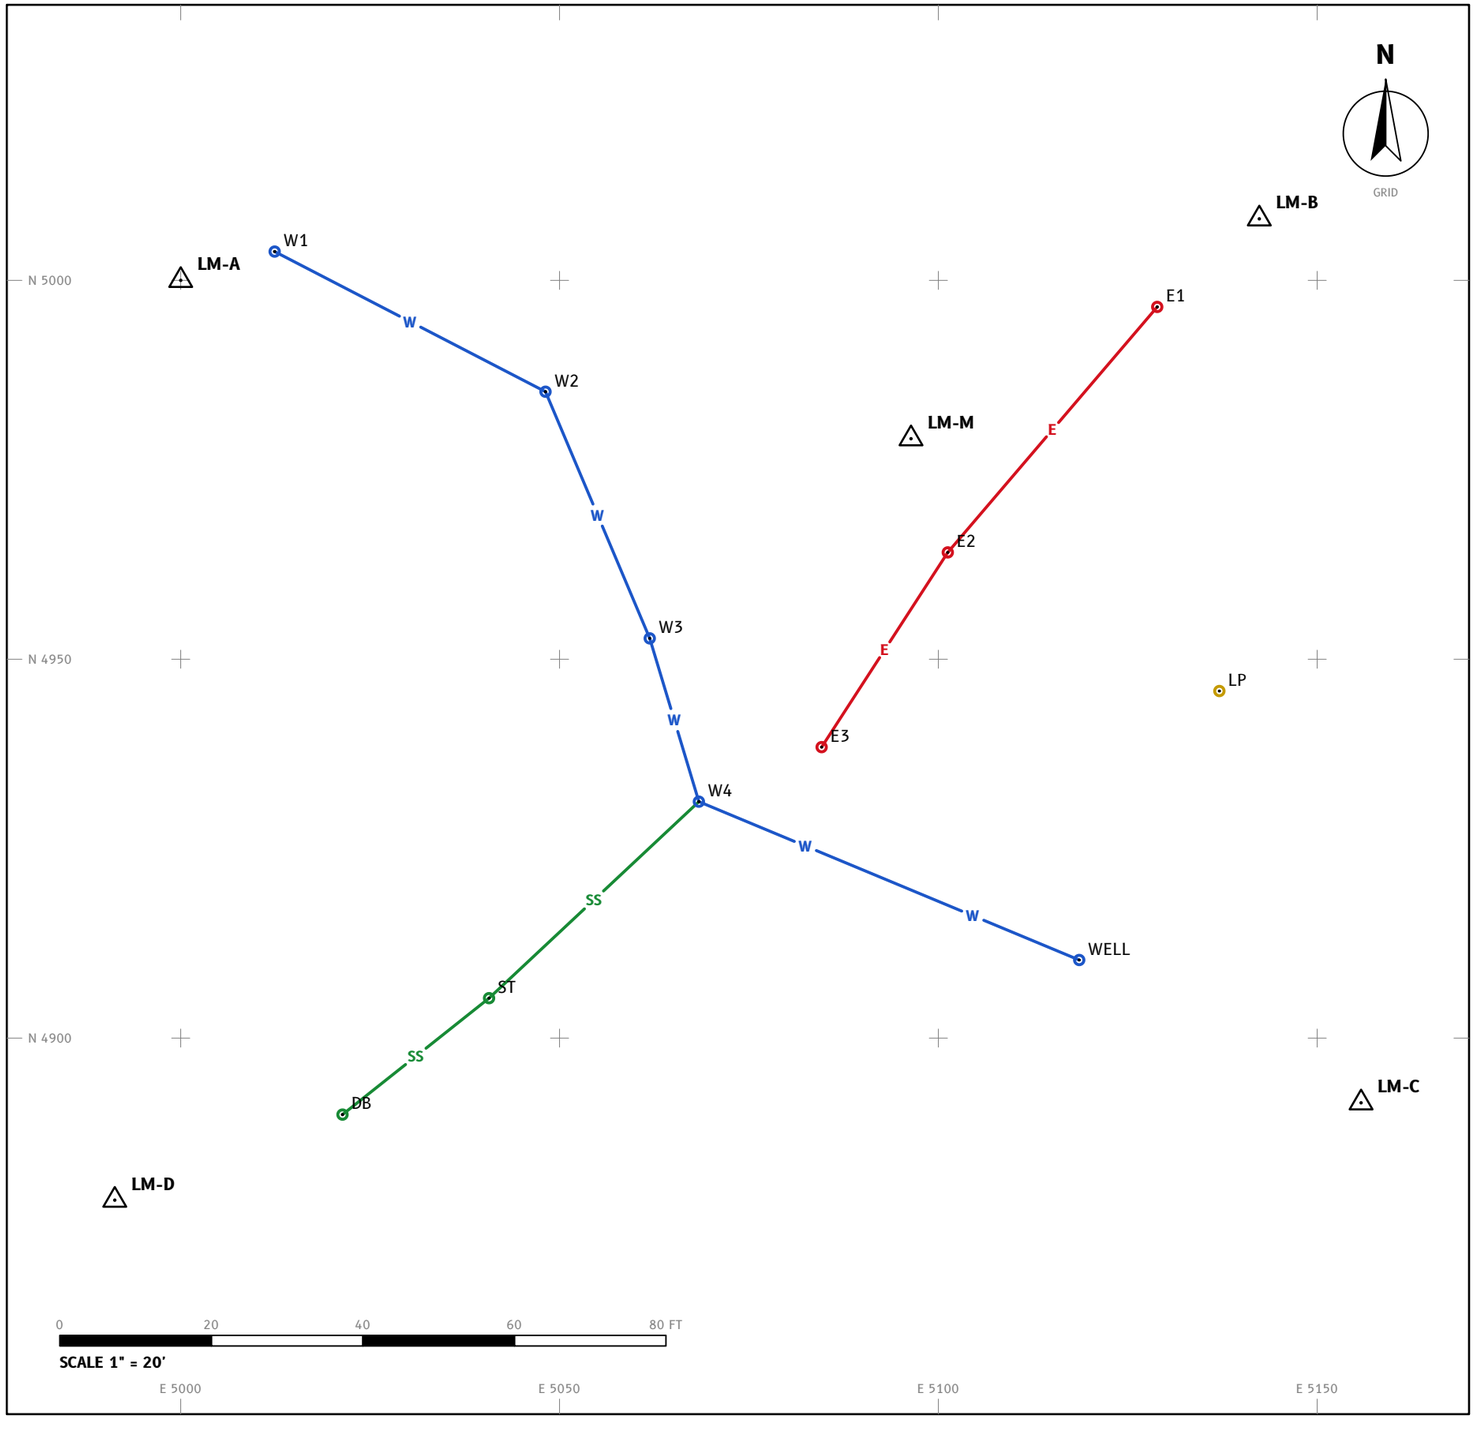

CONTROL (LANDMARKS)

NAME	NORTHING	EASTING	DESCRIPTION
LM-A	5000.00	5000.00	1/2" rebar with yellow cap, 2 ft E of driveway apron, NW corner
LM-B	5008.12	5142.36	1/2" rebar with yellow cap at NE fence corner post
LM-C	4891.46	5155.79	Chiseled X on concrete pad of shed, SE corner
LM-D	4878.61	4991.30	1/2" rebar with yellow cap, SW corner by garden
LM-M	4979.10	5096.39	16d nail in top of deck post, NW post of rear deck

POINTS

NAME	TYPE	NORTHING	EASTING	±95%	DEPTH
W1	Water	5003.80	5012.40	0.04	42 in
W2	Water	4985.30	5048.15	0.05	42 in
W3	Water	4952.75	5061.91	0.05	36 in
W4	Water	4931.20	5068.39	0.06	36 in
E1	Electric	4996.49	5128.89	0.08	30 in
E2	Electric	4964.10	5101.24	0.06	24 in
E3	Electric	4938.40	5084.59	0.06	24 in
ST	Sewer / septic	4905.27	5040.70	0.07	18 in to lid
DB	Sewer / septic	4889.90	5021.35	0.08	20 in
WELL	Water	4910.30	5118.59	0.09	
LP	Gas / oil	4945.80	5137.09	0.09	

NOTES

1. Local coordinates in feet: LM-A = N 5000.00, E 5000.00.
2. Basis of bearings: LM-A to LM-B = N 86°44'09" E.
3. Positions adjusted by least squares from 48 angles and 2 distances; angle reading precision 20". ± values are 95% radii (ft).
4. Coordinates are local (assumed). Bearings are referenced to the line LM-A to LM-B.
5. Depths are to top of pipe/conduit, measured when the trench was open.

PROJECT / PROPERTY

1234 EXAMPLE STREET

DRAWING TITLE

EXAMPLE PROPERTY — SITE SURVEY

DRAWN BY	DATE	SCALE
D. PANZINO	2026-10-15	1" = 20'

SIZE	DWG NO.	REV	SHEET
B	S-001	A	1 OF 1